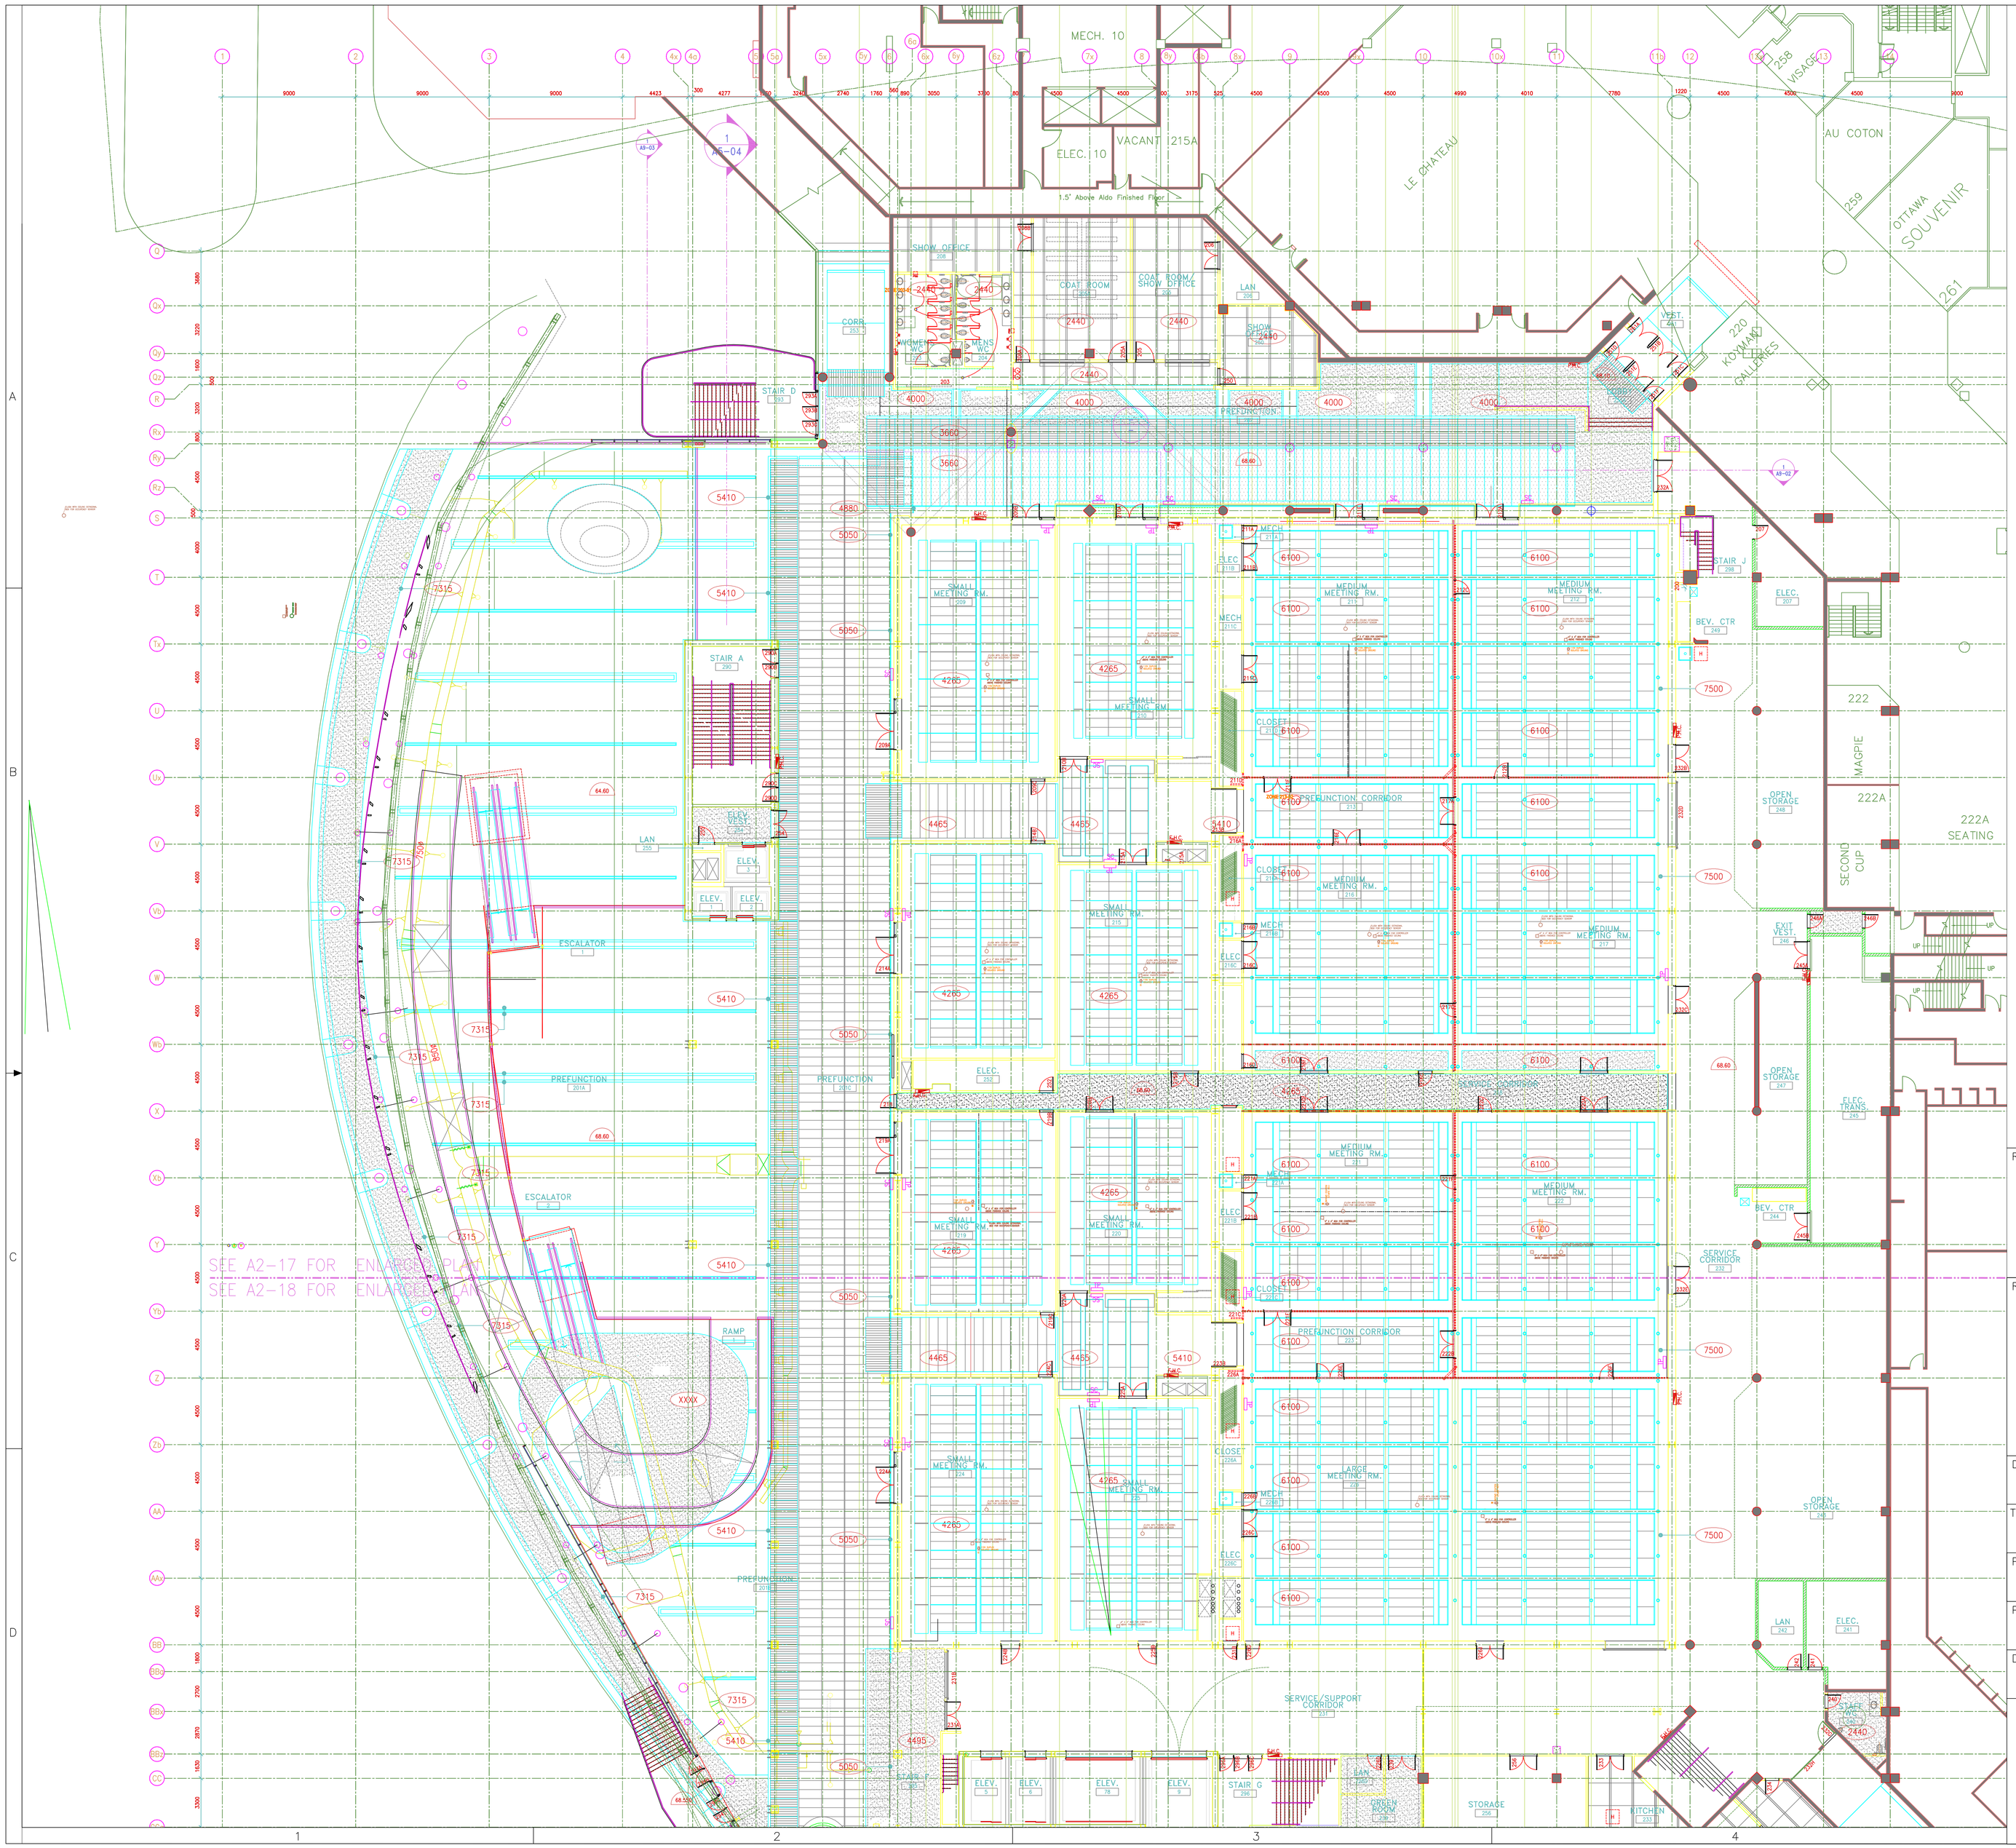

REFERENCE

REVISIONS

Rev 4, Changed Projector And Screens In Rooms
Rev 3, Showed Gridlines
Rev 2, Changed projector and screen locations
Rev 1, Separated Equipment on and above Ceiling
Rev 0, Preleminary
Not Approved for Construction

DATE:	VERIFIED BY:

TITLE: Second Floor Above Ceiling Audio Visual Equipment

PROJECT NO.:	ROOM Type: Second Floor Meeting Rooms

PROJECT NAME: Ottawa Convention Centre

DATE:	DRAWN BY:	DRAWING NO.:
Dec 13, 2010	VR	CE-02A

AVW·TELAV
Audio Visual Solutions
2365 MATHESON BLVD. EAST
TORONTO ONTARIO CANADA L4W 5B3
TEL.: (905) 366-9200, FAX: (905) 366-0274